


CONCEPT, NOT FOR FABRICATION


HeapLine · github.com/BoujeeEnjinia1701/heapline

REV	DESCRIPTION	DATE	BY
P1	Preliminary GA for TRL 3 (from cad/src/model.py)	2026-10-03	AC
P2	HPL-DDR-002: design for construction	2026-10-03	AC

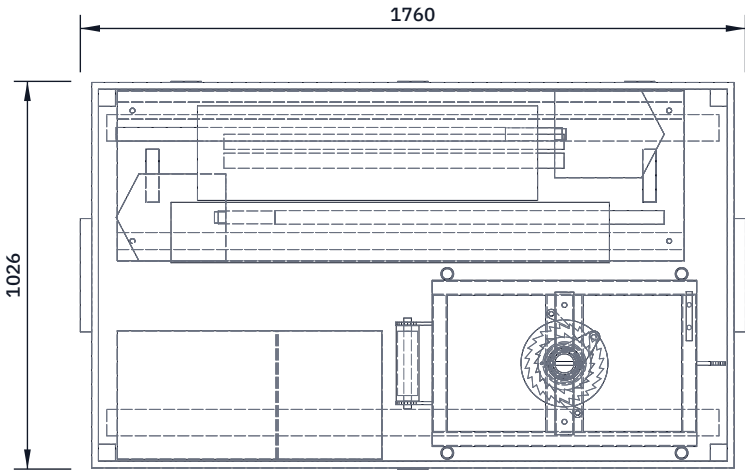


TOP VIEW

Scale 1:20; looking down (along -Z)

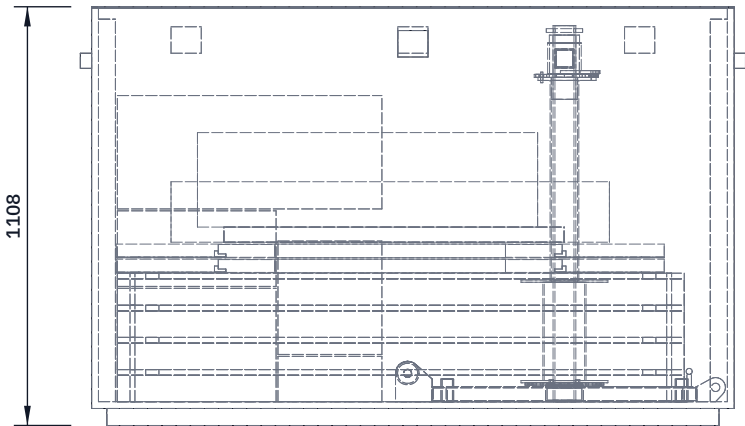


FRONT VIEW

Scale 1:20; looking at the front (along +Y)

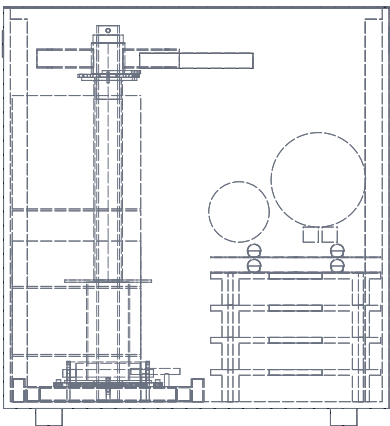

RIGHT VIEW

Scale 1:20; looking at the right side (along -X)

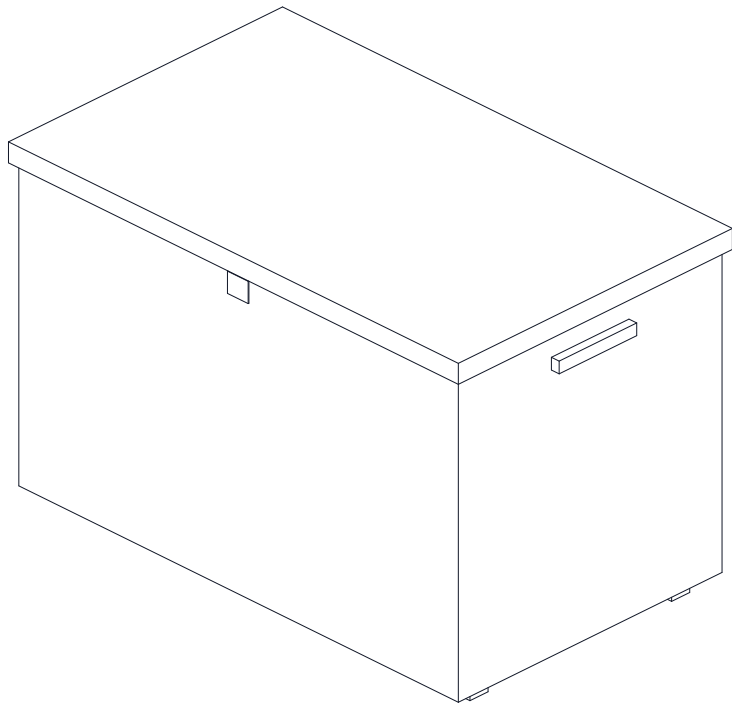

ISOMETRIC VIEW, LID CLOSED

Not to scale; seen from the front right

PACKING AND BOX (MM)

Box outside 1700 x 1020 x 1060 on skids; lid 1740 x 1060 (1, 2)

Inside 1664 x 984 x 1042; corner battens 45 x 45

Back: four crawl boards flat, 340 high (4)

On the boards: four shovels, probe bag, bars, rolled stretcher

Front right: capstan upright, bars off, stakes out (9 to 17)

Front left: rope, slings and clamp, stakes, lookout and PPE bags

Lid: drill card inside, stop rule outside (27)

Combination padlock on the front hasp (3)

Lid closed in the views; contents shown inside (top view)

Third-angle; front view from -Y; (n) = BOM line

HEAPLINE

github.com/BoujeeEnjinia1701/heapline

Site box: packed arrangement

DRAWING NO. HPL - DWG - 002			REV P2	SHEET 1 of 1	SIZE ANSI B
SCALE 1:20	UNITS mm	PROJECTION 	DATE 2026-10-03	DRAWN Amish Chadha	

MATERIAL / NOTES
18 mm exterior plywood box; contents per bom/bom.csv. PRELIMINARY, NOT FOR FABRICATION